# TRIPLE-EFFECT NAOH EVAPORATION PLANT — GENERAL ARRANGEMENT & ELEVATION VIEW

**SHOWING MULTI-TIER STEEL STRUCTURE, PIPING INTERCONNECTIONS, CONDENSER TOWER & BAROMETRIC SEAL PIT**

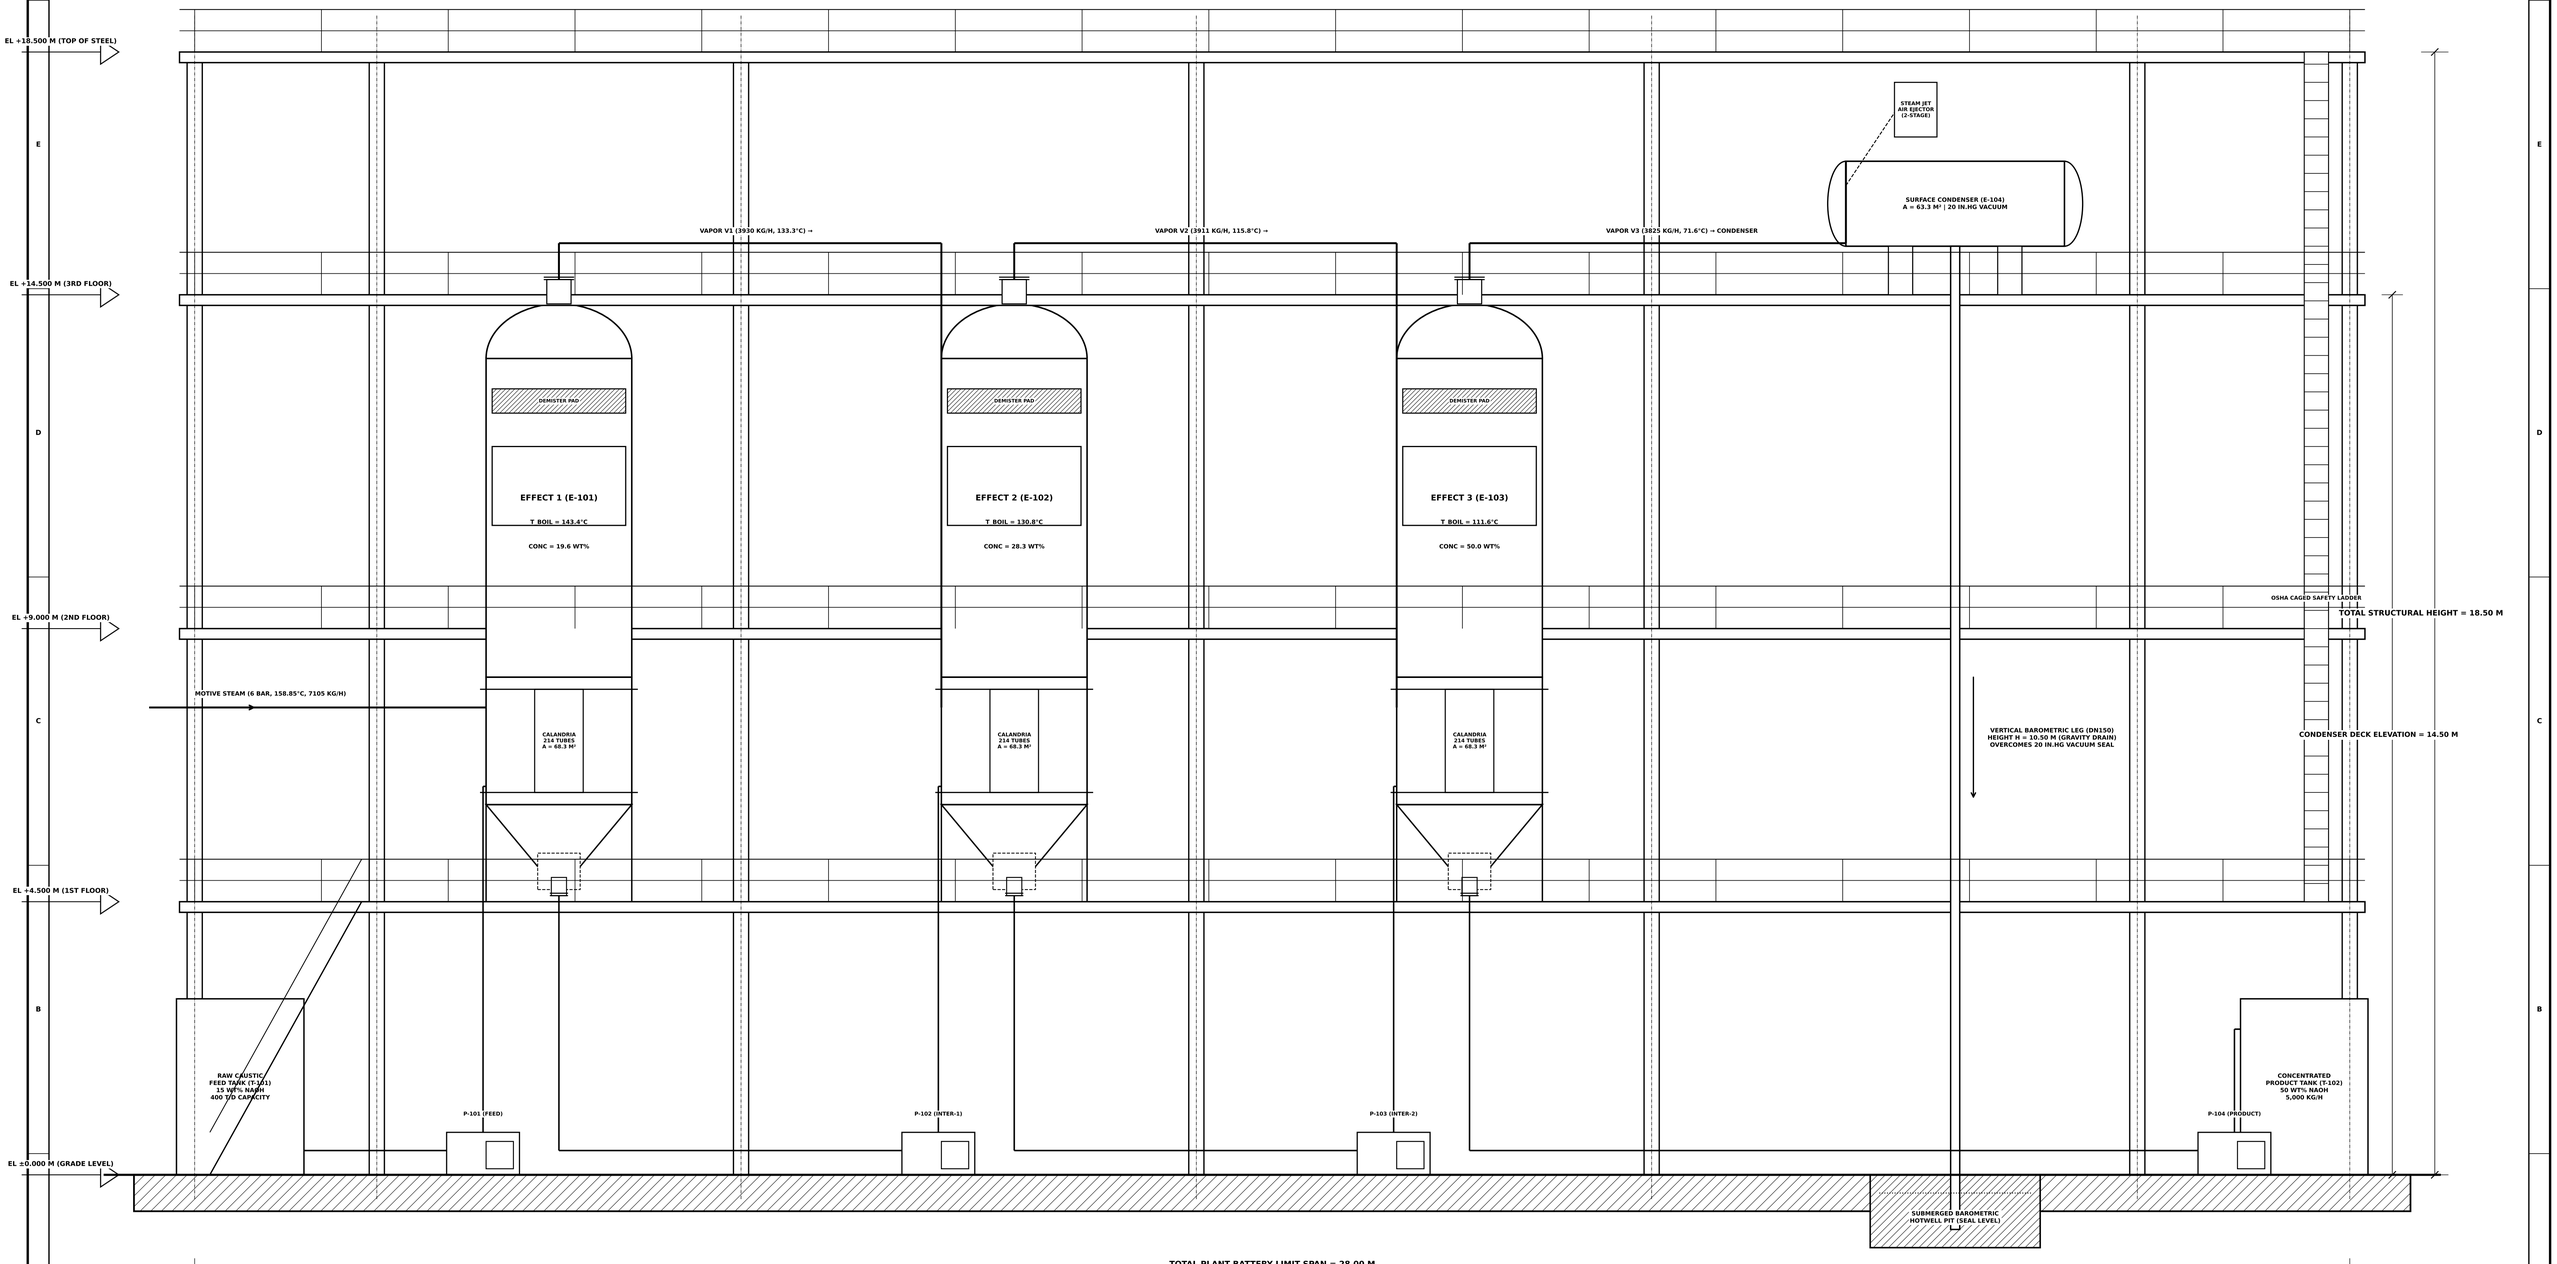


## OPTIONAL DIAGRAM 1 — PLANT GENERAL ARRANGEMENT & MULTI-TIER STRUCTURAL ELEVATION CAD

| | | | |
|---|---|---|---|
| **DRAWING TITLE**<br>PLANT ELEVATION GENERAL ARRANGEMENT (GA) | **SUBJECT**<br>PROCESS HEAT TRANSFER (PHT) | **COURSE / BRANCH**<br>B.E. CHEMICAL ENGINEERING | **SCALE**<br>1:50 METRIC / PROPORTIONED |
| **STUDENT NAME**<br>SOURISH SENAPATI | **EXAM ROLL NUMBER**<br>002310301035 | **ASSIGNED ROLL (LAST 2 DIGITS)**<br>35 (TARGET: 50.0 WT% NAOH PRODUCT) | **DATE**<br>01 / 09 / 2026 |
| **PLANT STRUCTURE TYPE**<br>4-TIER STRUCTURAL STEEL FRAMING (W12/ISMB300) | **TOTAL PLANT HEIGHT / SPAN**<br>TOTAL ELEVATION: +18.50 M \| BAY WIDTH: 28.00 M | **FEED CAPACITY / PRODUCT**<br>400 T/D (16,666.67 KG/H) FEED → 5,000 KG/H 50% NAOH | **BAROMETRIC SEAL HEIGHT**<br>H_LEG = 10.50 M (ATMOSPHERIC BAROMETRIC SEAL TO HOTWELL) |

**STANDARDS: OSHA 1910, ASME B73.1, ASME SEC VIII DIV 1 | STRUCTURAL STEEL: ASTM A36 / IS 2062 | ALL ELEVATIONS IN METERS (M)**